KOR STRUCTURAL · DRAFTING STANDARDS

Your standard details, in one Revit file

For Nelson Yu · from Ian Lalonde · 26 October

The standard details drafters place from Revit now come from your masters: your CAD typical-detail blocks and your Concrete Tower R24 template, in one file. Where a sheet of yours held a Revit copy of a CAD detail, it now holds the detail drawn from your CAD block, so a change you make in CAD is the one everybody gets. Everything else on your sheets is yours, untouched. This page is what you need to look at; the detail behind it is in the folder at the end.


FIRST: ABOUT AN HOUR AND A HALF, IN TWO SITTINGS

1. **Look at the 11 sheets that changed (about 30 minutes).** Folder file 2: each of your sheets on top, the same sheet in the new file underneath. On these 11 sheets, 59 details now come from your CAD blocks; the number and title in each position are yours and sit where you put them.
2. **Answer the 61 (about an hour and a quarter).** Folder file 1: 55 of the 190 CAD typical details have a Revit version in your templates that is drawn differently, and 6 details drafters had match only a view on no sheet in your templates, drawn differently. One tick each. Until you have answered, those details stay out of the drafters' palette.

WHAT IS IN THE FILE

WHAT	HOW MANY	WHERE IT CAME FROM
Your own drafting views	550	Your Concrete Tower R24 template, every one that sits on one of your sheets (550 of 550 on a sheet).
Details from your CAD blocks	190 + 41	All 190 typical details on the big sheet, brought in by the CAD Detail button; 41 more copies of them fill positions on your sheets.
Your notes and schedules, placeable	117	A detail-view copy of each of your 118 legends (one is empty), named "<legend> - DETAIL VIEW", printing identically to the legend. The palette cannot place a legend; it can place these.
Details drafters had, from your off-sheet views	10	12 details the old catalogue offered exist in your templates only as views on no sheet; the identical ones were copied in (three numbers shared one drawing).
Details drafters had, from the August R25 file	53	54 details the old catalogue offered exist only in the August R25 file (37 wood, 16 steel, 1 concrete). Each was brought in from that file by the CAD Detail button and looked at beside the old picture and the R25 view: the same drawing. Two old names match nothing there (an empty column schedule; a view titled only "TYPICAL DETAIL").
Sheets and legends	90 · 118	Yours, as in the template.
The file	`\\Kor-fs01\Drafting\KOR-Standards\template\MASTER\KOR-Standard-Details-R24.rvt` Revit 2024. The previous master (`KOR-Standards-Master-R25.rvt`) stays beside it, untouched.	

How it was checked: every one of the 190 printed from Revit beside its CAD plot under KOR.ctb and looked at; 181 of 190 match word for word and line for line, 9 differ in text only (font, the diameter symbol, spacing); 190 of 190 dashed at CAD's length.

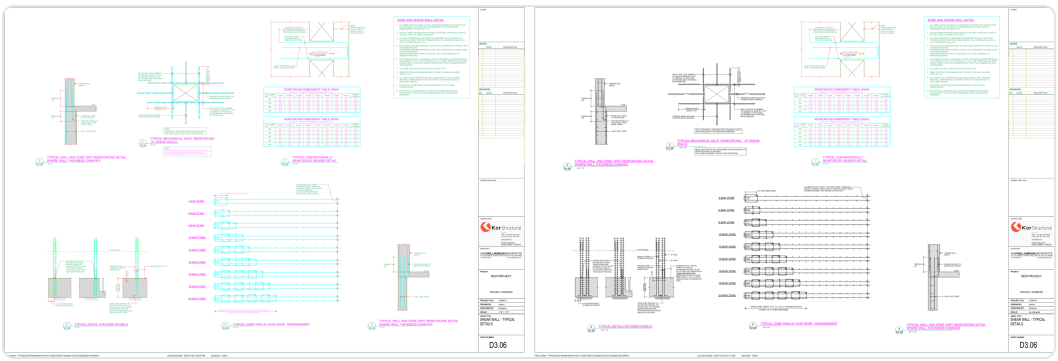

D3.06, shear wall typical details. Left: your sheet. Right: the same sheet in the new file. Five details now come from your CAD blocks (black); the zone and shear wall notes and the two embedment tables are yours, unchanged. All 11 changed sheets are in folder file 2.

DECISIONS THAT ARE YOURS

QUESTION	WHAT WE FOUND	YOUR ANSWER
The 55 that differ	CAD and Revit versions drawn differently, one page each (folder file 1).	CAD right / Revit newer / both wrong, per page.
The Revit font for CAD's SHX text	9 of the 190 differ in text only. One, D503-13 (romans.shx), prints thin and crowded in Revit: worth fixing in the CAD block itself.	Pick the font; say whether D503-13 is redrawn.
One title moved	On D3.05, S3.05 and 1E3.05, "Diagonally reinforced header section" ran into detail 1 at your title position (the CAD drawing is a little larger), so it was moved under its drawing.	Keep it, or say where it goes.
The wood "framing over" sheet	Decided as assumed, below.	Confirm, or overrule.
An old firm name	Your off-sheet view "Typical Shearwall Details" still reads "confirm with JOHN BRYSON & PARTNERS" at the mechanical-hole note; the old catalogue's version read "KOR STRUCTURAL".	Fix the view in your template.
Three R25 views with overlapping text	"DEEP BEAM POCKET DETAIL 1", "DEEP BEAM POCKET DETAIL 2" and "ENTRY POST DETAIL" have their notes drawn over one another in the August R25 file itself, so they read the same way in the new file.	Redraw them, or say they are not standards.

WOOD FRAMING: THE ONE WAY, DECIDED AS ASSUMED – YOU CONFIRM

Ian has settled how wood framing is drawn. His words, 25 October:

> "I think the issue is that until recently we were told woodframe couldn't be done in revit" · "If we CAN then 2D cad is redundant" · "I don't want THREE versions ... make some decisions and we simply note them as assumed and need confirmation."

So framing plans show modelled members (beams, joists, posts, hold-downs, walls), with 2D for annotation only. Standard details, the typical sections and connections, stay 2D and are not affected. For the **"Level N showing Level N+1 framing over" sheet** the office now has one way, recorded on 26 October as assumed with your name against it: a ceiling plan of level N carries the framing over, beside the engineering plan of level N+1, two plan views a sheet, at 1/8" = 1'-0" (the scale of the office concrete plans); the view type is **## - WD_STRUCTURAL WITH FRAMING OVER** and the per-level templates **## - WD_Structural with Framing Over Level N**, the names in your Wood Framing View Setup (July 2025), to be generated into the office template; the naming prefix is "## -" throughout. That is Edgar's make (31165-01) under your own names, chosen over Sherwood's (two plans of a foundation view type at 3/16", 21 per-level templates) and over the standard file's S2.13, which is legends with no plan view.

WHAT REVIT DOES DIFFERENTLY, SO YOU KNOW BEFORE YOU LOOK

LIMIT	WHERE YOU'D SEE IT
Small circles print as many-sided polygons	Revit's PDF print, not the conversion: the file holds true circles. Bolt holes in D201-07, about 3 mm on paper.
Dense hatch in a thin band prints solid	4 details: D201-07 and D503-15 (HSS walls), D502-30 and D502-31 (paver band at slab level).
Symbols inside a linetype	The W.W.M. line's X marks are not drawn in Revit; one line in D504-20.
Placing in Revit 2026	The file is Revit 2024. A drafter in 2026 waits about two minutes the first time the palette places a detail after a template update (a message says so); after that a placement takes seconds. No prompt; the file is never changed.

THE DETAIL BEHIND THIS PAGE

One folder, nothing attached: `\\Kor-fs01\Drafting\KOR-Standards\for-review\2026-10-26 Nelson standards package`

- **1** — the 55 details drawn differently in CAD and Revit, one page each, with the answer line. Each page also says where that Revit version stands in the new file: not in it (32), replaced on your sheet by a CAD detail (13), or in it beside the CAD one (10). Plus 6 pages: details drafters had whose only match in your templates is an off-sheet view drawn differently.
- **2** — your 11 changed sheets, yours above the new file's.
- **3** — all 190 CAD details, the CAD plot beside the Revit print, with the measured check on each.